
MAUREL'EC

Plan d'implantation électrique – Appartement T4 (97,57 m² + 2 balcons)

Appareillage Legrand Céliane with Netatmo – NF C 15-100 – Le numéro à côté de chaque symbole renvoie au circuit du tableau.

Plan redessiné d'après le plan commercial, cotes approximatives – implantation indicative à valider sur place.

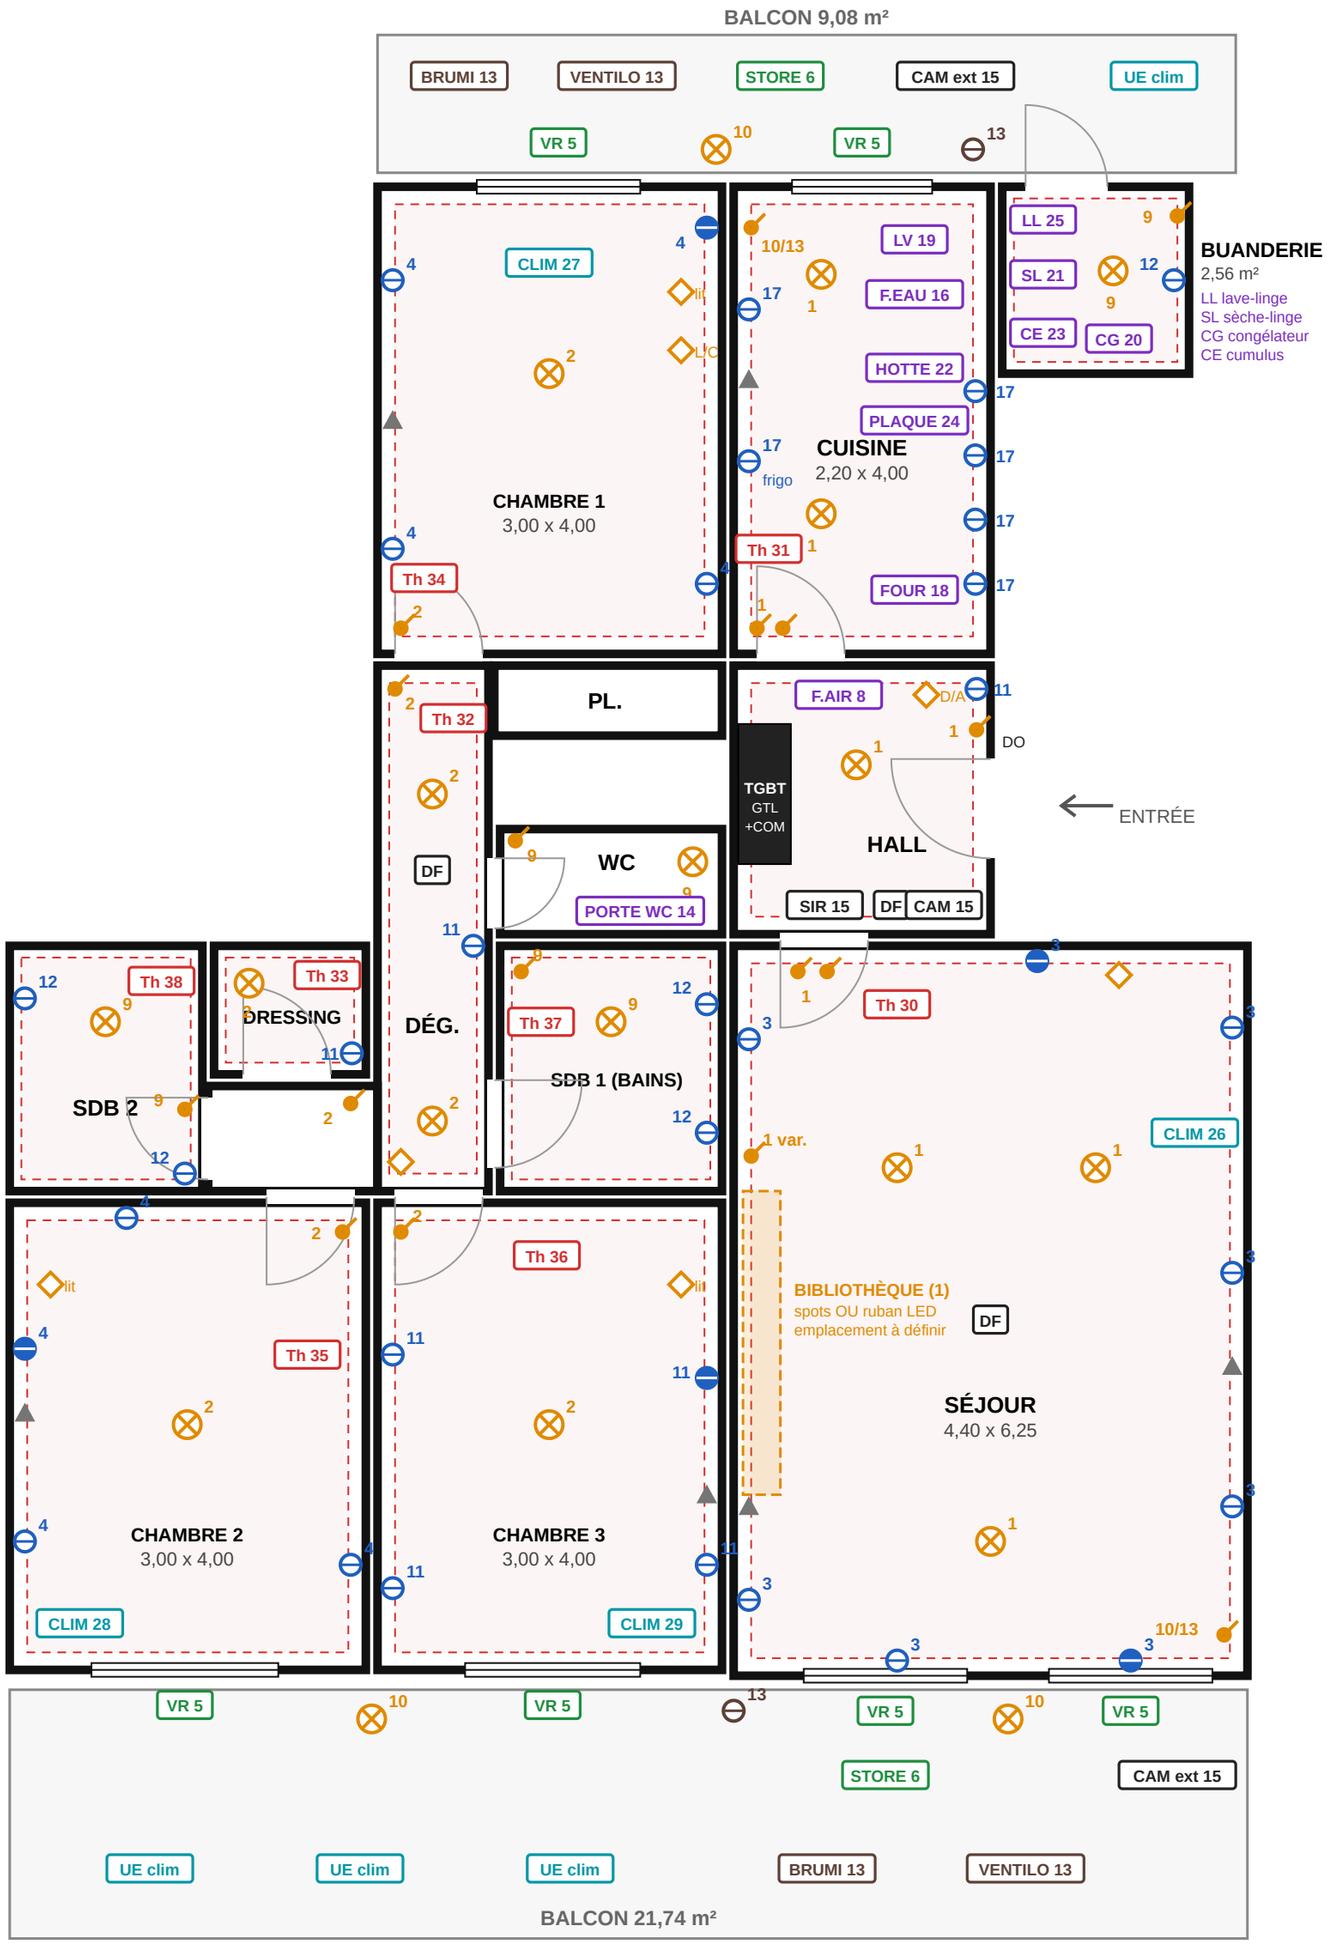

LÉGENDE

- Point lumineux DCL
- Interrupteur connecté Céliane with Netatmo (10/13 = cdes balcon)
- Commande sans fil (lit, D/A = Départ/Arrivée + volets, L/C = Lever/Coucher)
- Prise 16 A 2P+T Céliane
- Prise connectée Céliane with Netatmo
- Prise étanche Plexo IP55 (balcons)
- Prise RJ45 grade 3TV
- LV — Prise spécialisée / sortie de câble
- VR — Volet roulant / store connecté (alim + cde Céliane)
- CLIM — Clim réversible (UE = unité extérieure)
- Th — Thermostat connecté plancher chauffant
- Zone de plancher chauffant électrique
- DF — Détecteur de fumée connecté (pile)
- CAM — Caméra / SIR = sirène / DO = détect. ouverture

CIRCUITS DU TABLEAU

ID1 40A A

1 Éclairage jour + bibliothèque – 10A
2 Éclairage nuit – 10A
3 Prises séjour – 20A
4 Prises chambres 1 et 2 – 16A
5 Volets roulants – 16A
6 Stores – 16A
7 Coffret communication – 16A
8 Filtre à air – 2A

ID2 40A A

9 Éclairage SDB, WC, buanderie – 10A
10 Éclairage balcons – 10A
11 Prises ch.3, hall, dég., dressing – 16A
12 Prises SDB 1-2, buanderie – 16A
13 Balcons : prises, brumi, ventilo – 16A
14 Porte électrique WC – 16A
15 Alarme / caméras – 16A
16 Filtre à eau – 16A

ID3 40A A

17 Prises cuisine + frigo – 20A
18 Four – 20A
19 Lave-vaisselle – 20A
20 Congélateur (buanderie) – 20A
21 Sèche-linge (buanderie) – 20A
22 Hotte – 16A
23 Cumulus (contacteur J/N) – 20A

ID4 40A F

24 Plaque de cuisson – 32A
25 Lave-linge (buanderie) – 20A
26 Clim séjour – 20A
27 Clim chambre 1 – 20A
28 Clim chambre 2 – 20A
29 Clim chambre 3 – 20A

ID5 63A A

30 Plancher séjour – 16A
31 Plancher cuisine – 16A
32 Plancher hall/dég. – 16A
33 Plancher buand./dressing – 16A

ID6 63A A

34 Plancher chambre 1 – 16A
35 Plancher chambre 2 – 16A
36 Plancher chambre 3 – 16A
37 Plancher SDB 1 – 16A
38 Plancher SDB 2 – 16A