
MAUREL'EC

Électricité générale · maurelec.btp@gmail.com · 06 12 31 67 03

Plan d'implantation électrique – Avant-projet

Client : M. Augustin Fuentes · Appartement T3 ~68 m² · Nice Saint-Roch · Octobre 2026

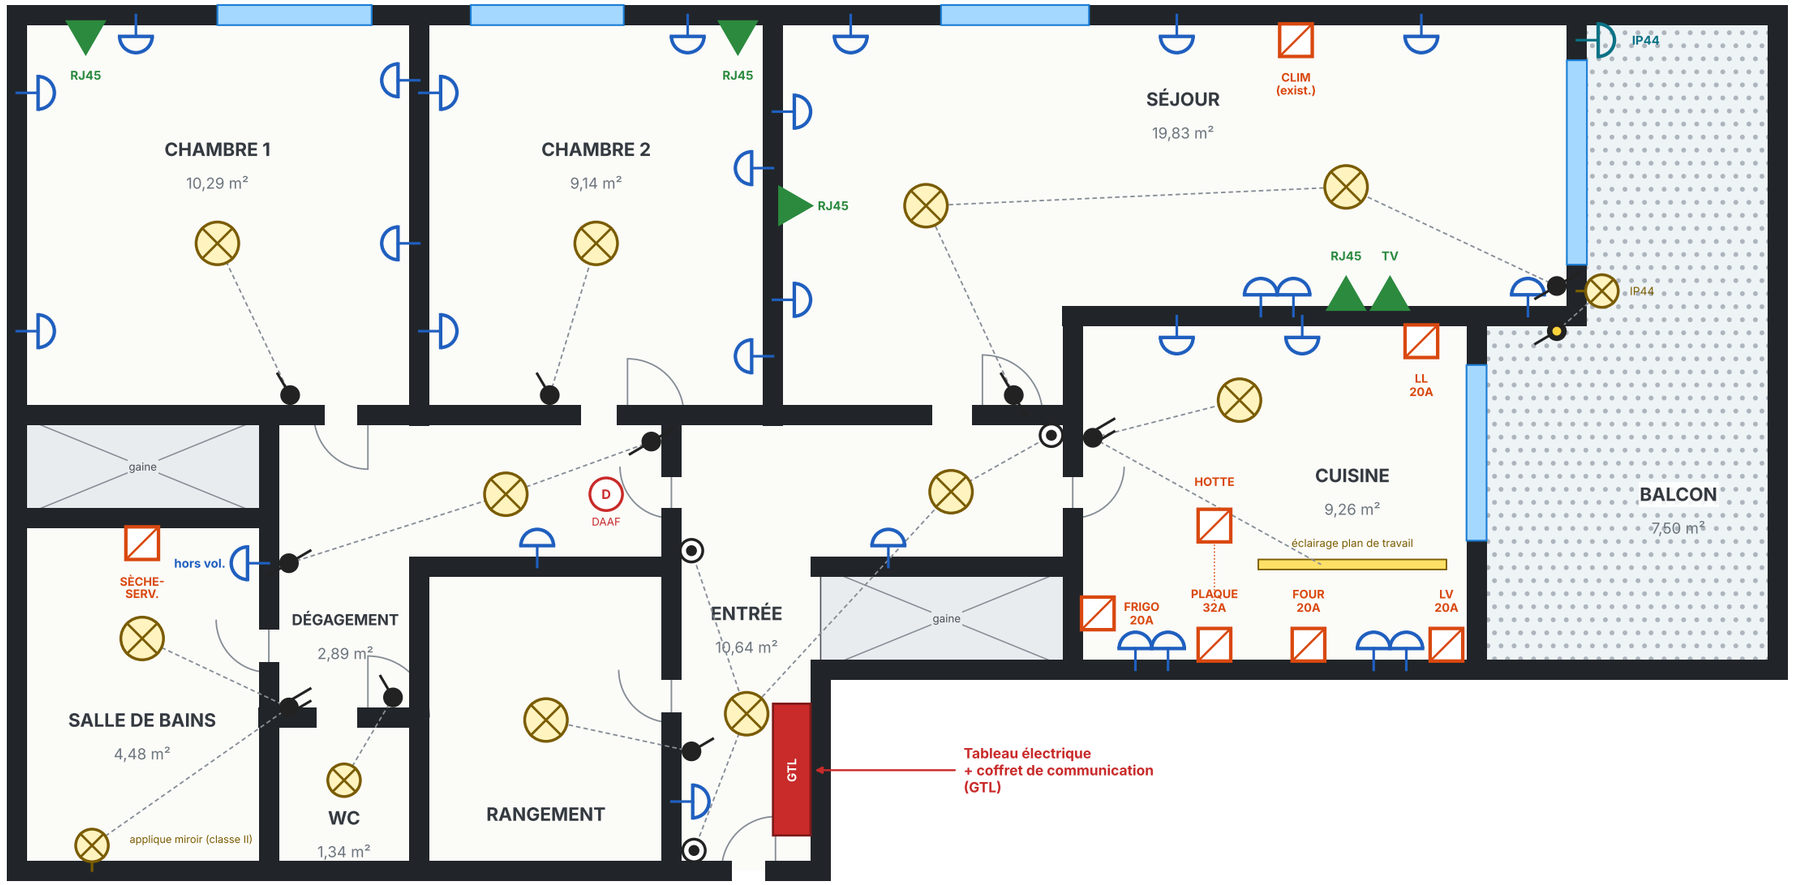

← façade / fenêtres en haut du plan · balcon à droite · palier en bas →

LÉGENDE

- Prise de courant 16 A 2P+T
- Prise double 16 A 2P+T
- Prise étanche IP44 (balcon)
- Circuit spécialisé / sortie de câble
- Prise RJ45 cat. 6 / prise TV
- Point lumineux plafond (DCL)
- Applique murale (DCL)
- Interrupteur simple allumage
- Interrupteur double allumage
- Interrupteur va-et-vient
- Interrupteur à voyant
- Bouton poussoir (télérupteur)
- Détecteur de fumée (DAAF)
- Tableau électrique / GTL
- Liaison commande → éclairage

Abréviations : LV lave-vaisselle · LL lave-linge · CLIM climatisation existante (à vérifier) · hors vol. = hors volumes de la salle de bains

MAUREL'EC

Électricité générale · maurelec.btp@gmail.com · 06 12 31 67 03

Plan d'implantation électrique – Avant-projet

Client : M. Augustin Fuentes · Appartement T3 ~68 m² · Nice Saint-Roch · Octobre 2026

1. Équipements par pièce

Pièce	Prises 16 A	Circuits spécialisés	RJ45 / TV	Éclairage	Remarques
Séjour	8	–	2 + 1 TV	2 DCL (va-et-vient)	Alim. clim existante à vérifier
Chambre 1	5	–	1	1 DCL	
Chambre 2	5	–	1	1 DCL	
Cuisine	6 (dont 4 sur plan de travail)	Plaque 32A, four, LV, LL, frigo, hotte	–	1 DCL + plan de travail	Positions selon plan cuisiniste
Entrée / couloir	2	–	–	2 DCL (télérupteur, 3 BP)	GTL : tableau + coffret com.
Dégagement	1	–	–	1 DCL (va-et-vient)	Détecteur de fumée
Salle de bains	1 (hors volumes)	Sèche-serviettes	–	1 DCL + applique miroir	Liaison équipotentielle
WC	–	–	–	1 DCL	
Rangement	–	–	–	1 DCL	
Balcon	1 étanche IP44	–	–	1 applique IP44 (voyant)	
TOTAL	**29 prises**	**8 circuits**	**4 RJ45 + 1 TV**	**13 points lumineux**	

2. Tableau électrique proposé (3 rangées · 13 modules, réserve ≥ 20 %)

ID1 · 63 A 30 mA type A

N°	Circuit	Disj.	Section
1	Plaque de cuisson induction	32 A	6 mm²
2	Lave-linge	20 A	2,5 mm²
3	Prises chambres 1 et 2 (10 PC)	20 A	2,5 mm²
4	Éclairage nuit (chambres, dégagement, SdB, WC, rangement)	10 A	1,5 mm²
5	Sèche-serviettes	16 A	1,5 mm²

ID2 · 40 A 30 mA type A

N°	Circuit	Disj.	Section
6	Four	20 A	2,5 mm²
7	Lave-vaisselle	20 A	2,5 mm²
8	Réfrigérateur	20 A	2,5 mm²
9	Prises cuisine plan de travail (6 PC)	20 A	2,5 mm²
10	Hotte	16 A	1,5 mm²

ID3 · 40 A 30 mA type A

N°	Circuit	Disj.	Section
11	Prises séjour (8 PC)	20 A	2,5 mm²
12	Prises entrée, dégagement, SdB, balcon (5 PC)	20 A	2,5 mm²
13	Éclairage jour (séjour, entrée, cuisine, balcon)	10 A	1,5 mm²
14	Climatisation (existante – à vérifier)	20 A	2,5 mm²
15	Coffret de communication (VDI)	2 A	1,5 mm²

3. Points complémentaires

- Dépose / condamnation de l'ancienne installation (tableau à fusibles, goulottes apparentes).
- Distribution des circuits dans le faux plafond technique (6 à 8 cm) avec descentes encastrées dans les cloisons ; solutions discrètes (moulures / plinthes techniques) sur les murs béton.
- Mise à la terre : contrôle de la prise de terre et de la liaison équipotentielle principale ; liaison équipotentielle locale en salle de bains.
- Coffret de communication grade 2 TV dans la GTL : 4 prises RJ45 cat. 6 (séjour ×2, chambres ×1) + 1 prise TV.
- Repérage complet du tableau, essais (isolement, continuité, déclenchement des différentiels) et remise du schéma.
- Options possibles : prises USB en chevet, éclairage LED encastré en faux plafond, interrupteurs connectés, prise recharge balcon.

Implantation indicative établie d'après le croquis du diagnostic (réf. 2139 C) – cotes non contractuelles. Positions définitives à valider avec le client lors de la visite et selon le plan de cuisine / salle de bains. Installation conforme NF C 15-100.